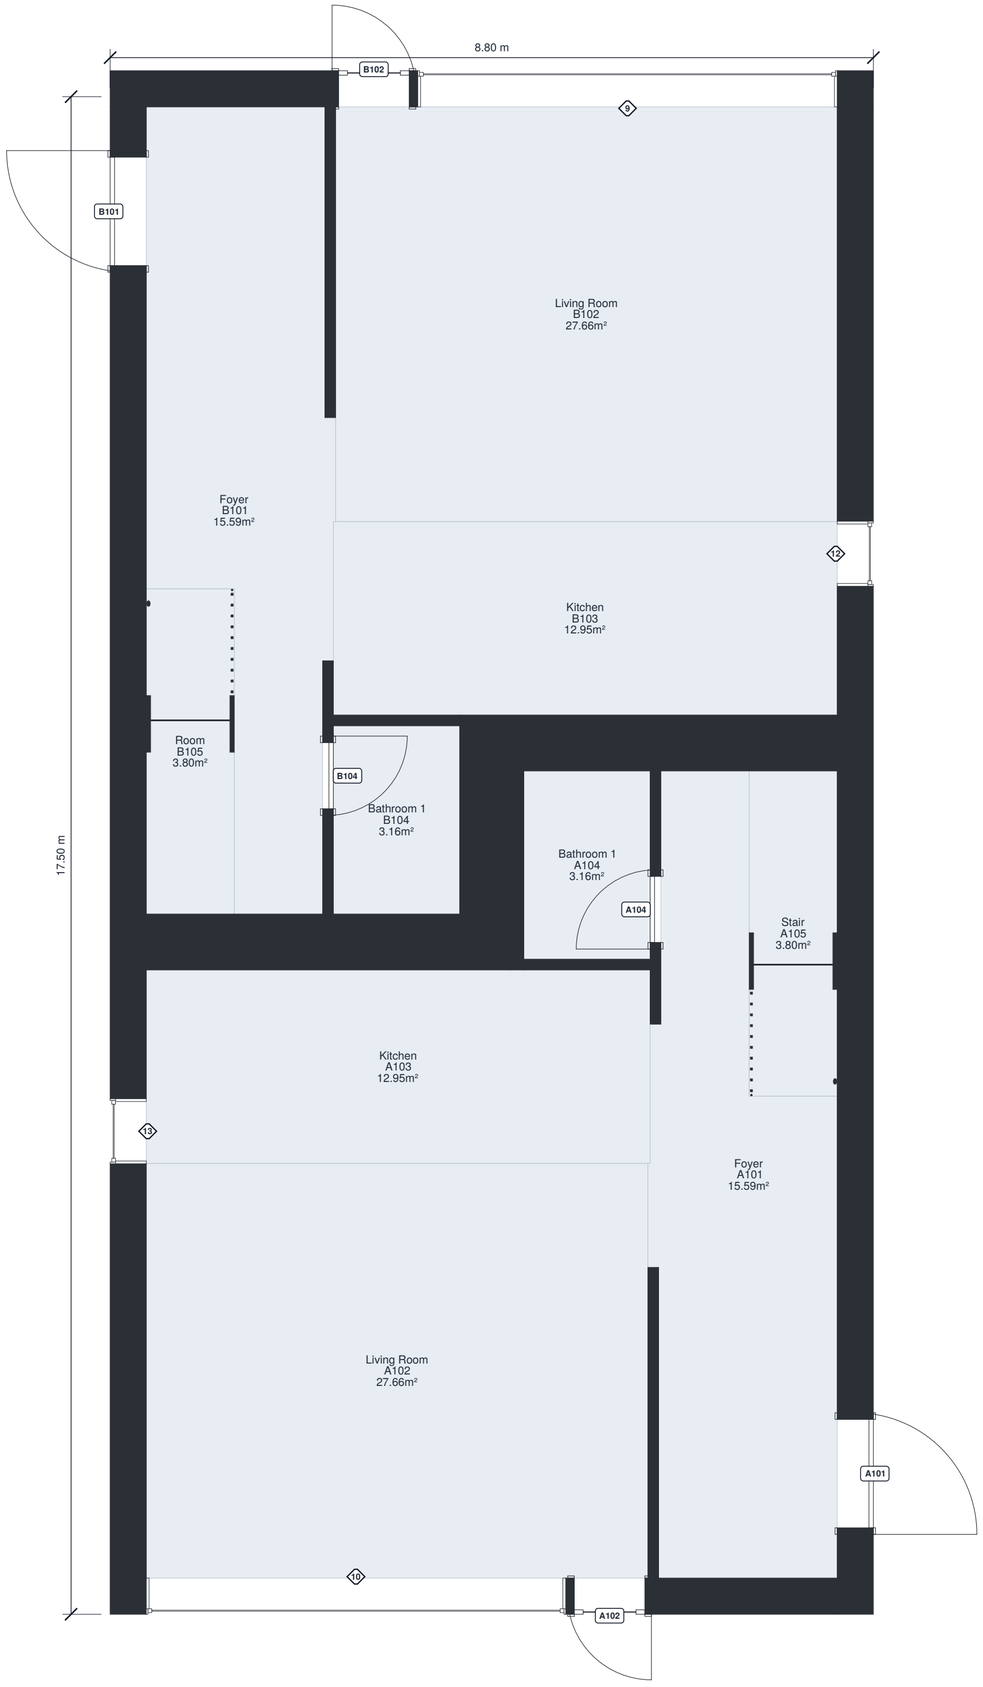

CODE REVIEW 3D · SAMPLE MODEL

Duplex Apartment

Residential

SHEET

Level 1 floor plan

SHEET NO.

A-101

of 6 sheets

SCALE

1:50 at A2

0 1 2 5 m

N

LEVEL DATA

Floor elevation	**0.00 m**
Floor to floor	**3.10 m**
Plan cut height	**1.2 m above floor**
Rooms	**10**
Net room area	**141.8 m²**
Doors / windows	**6 / 4**
Overall (walls)	**8.80 × 17.50 m**

LEGEND

Walls and columns cut at 1.2 m	**dark fill**
Room: name, number, area (m²)	**light fill**
Door tag, see door schedule	**mark in box**
Window tag, see window schedule	**mark in hexagon**

SOURCE

BSI (2020) "Duplex Apartment Test Files," buildingSMART International. License: CC BY 4.0.

Changes: drawings generated from the 3D model (duplex.ifc); the model itself is unchanged.

NOTES

Generated automatically from the IFC model for review demos. Not a construction document. Check the scale bar before measuring from a print.

Generated 2026-10-24 with IfcOpenShell
apps/review/scripts/make_drawings.py