
Duplex Apartment

Residential · drawings generated from the IFC model

SHEET INDEX

G-001	Cover sheet and sheet index	—
A-101	Level 1 floor plan	1:50
A-102	Level 2 floor plan	1:50
A-601	Room schedule	—
A-611	Door schedule	—
A-621	Window schedule	—

KEY PLAN · LEVEL 1 FLOOR PLAN · NOT TO SCALE

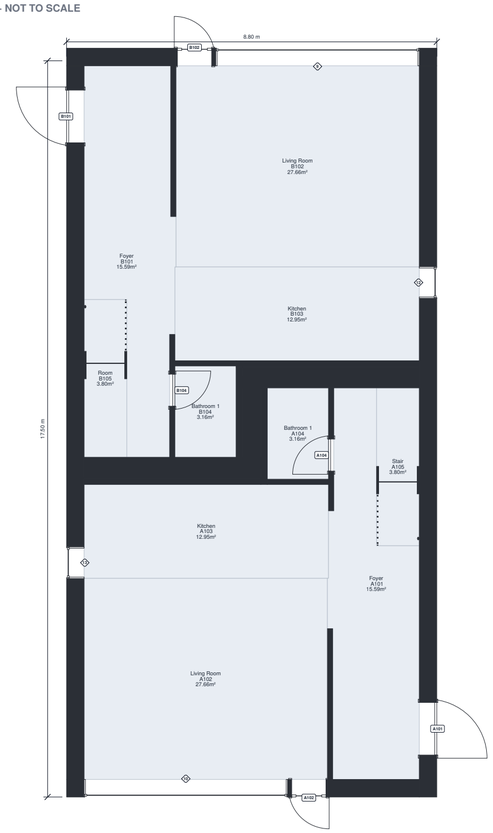

BUILDING DATA

Storeys in model	**T/FDN, Level 1, Level 2, Roof**
T/FDN: elevation	**-1.25 m**
Level 1: elevation	**+0.00 m**
Level 2: elevation	**+3.10 m**
Roof: elevation	**+6.00 m**
Rooms on floors	**20**
Net room area, floors	**276.3 m²**
Net area, Level 1	**141.8 m²**
Net area, Level 2	**134.5 m²**
Doors (external)	**14 (4)**
Windows	**24**

SOURCE MODEL

File	**duplex.ifc**
Schema	**IFC2X3**
Exported	**2011-09-07**
Authoring	

20100326_1700 Autodesk Revit Architecture 2011 - 1.0

ABOUT THESE DRAWINGS

Plans are cut from the 3D model 1.2 m above each floor.
Schedules list the model's own property values.
Tags on plans match the Mark column of the schedules.
Roof and foundation levels have no plan sheet.

CODE REVIEW 3D · SAMPLE MODEL

Duplex Apartment

Residential

SHEET

Cover sheet and sheet index

SHEET NO.

G-001

of 6 sheets

SCALE

Not to scale

SET

Sheets	**6**
Paper	**A2**

SOURCE


BSI (2020) "Duplex Apartment Test Files," buildingSMART International. License: CC BY 4.0.

Changes: drawings generated from the 3D model (duplex.ifc); the model itself is unchanged.

NOTES

Generated automatically from the IFC model for review demos. Not a construction document. Check the scale bar before measuring from a print.

Generated 2026-10-24 with IfcOpenShell
apps/review/scripts/make_drawings.py

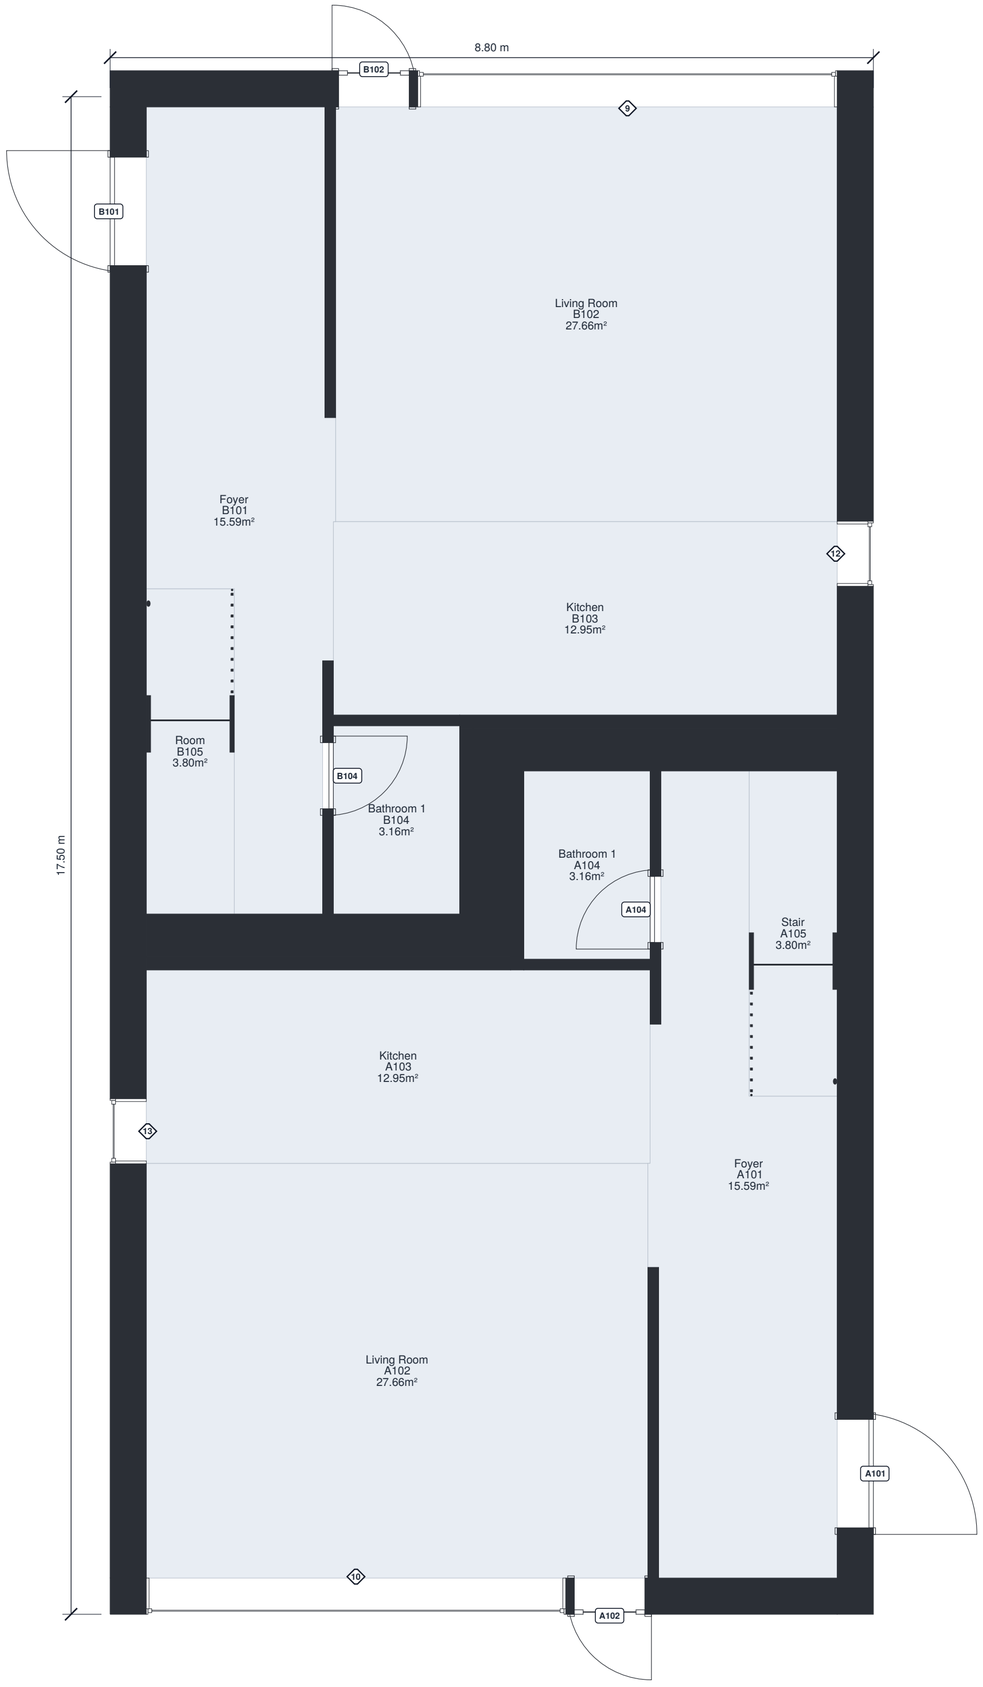

CODE REVIEW 3D · SAMPLE MODEL

Duplex Apartment

Residential

SHEET

Level 1 floor plan

SHEET NO.

A-101

of 6 sheets

SCALE

1:50 at A2

0 1 2 5 m

N

LEVEL DATA

Floor elevation	**0.00 m**
Floor to floor	**3.10 m**
Plan cut height	**1.2 m above floor**
Rooms	**10**
Net room area	**141.8 m²**
Doors / windows	**6 / 4**
Overall (walls)	**8.80 × 17.50 m**

LEGEND

Walls and columns cut at 1.2 m	**dark fill**
Room: name, number, area (m²)	**light fill**
Door tag, see door schedule	**mark in box**
Window tag, see window schedule	**mark in hexagon**

SOURCE

BSI (2020) "Duplex Apartment Test Files," buildingSMART International. License: CC BY 4.0.

Changes: drawings generated from the 3D model (duplex.ifc); the model itself is unchanged.

NOTES

Generated automatically from the IFC model for review demos. Not a construction document. Check the scale bar before measuring from a print.

Generated 2026-10-24 with IfcOpenShell
apps/review/scripts/make_drawings.py



CODE REVIEW 3D · SAMPLE MODEL

Duplex Apartment

Residential

SHEET

Level 2 floor plan

SHEET NO.

A-102

of 6 sheets

SCALE

1:50 at A2

0 1 2 5 m

N

LEVEL DATA

Floor elevation	**3.10 m**
Floor to floor	**2.90 m**
Plan cut height	**1.2 m above floor**
Rooms	**10**
Net room area	**134.5 m²**
Doors / windows	**8 / 18**
Overall (walls)	**8.80 × 17.51 m**

LEGEND

Walls and columns cut at 1.2 m	**dark fill**
Room: name, number, area (m²)	**light fill**
Door tag, see door schedule	**mark in box**
Window tag, see window schedule	**mark in hexagon**

SOURCE

BSI (2020) "Duplex Apartment Test Files," buildingSMART International. License: CC BY 4.0.

Changes: drawings generated from the 3D model (duplex.ifc); the model itself is unchanged.

NOTES

Generated automatically from the IFC model for review demos. Not a construction document. Check the scale bar before measuring from a print.

Generated 2026-10-24 with IfcOpenShell
apps/review/scripts/make_drawings.py

ROOM SCHEDULE

Number	Name	Level	Area (m²)	Perimeter (m)	Height (m)	Volume (m³)	Category	Occupancy zone
A101	Foyer	Level 1	17.94	24.22	2.60	40.2	General Residential Space	Unit A OccupancyZoneName
A102	Living Room	Level 1	30.14	22.03	2.60	71.4	Living Spaces	Unit A OccupancyZoneName
A103	Kitchen	Level 1	13.90	16.42	2.60	33.5	Kitchen	Unit A OccupancyZoneName
A104	Bathroom 1	Level 1	4.00	8.20	2.60	8.2	Bathroom	Unit A OccupancyZoneName
A105	Stair	Level 1	4.92	10.50	5.70	20.8	Stairway	Unit A OccupancyZoneName
B101	Foyer	Level 1	17.94	24.22	2.60	40.2	General Residential Space	Unit B OccupancyZoneName
B102	Living Room	Level 1	30.14	22.03	2.60	71.4	Living Spaces	Unit B OccupancyZoneName
B103	Kitchen	Level 1	13.90	16.42	2.60	33.5	Kitchen	Unit B OccupancyZoneName
B104	Bathroom 1	Level 1	4.00	8.20	2.60	8.2	Bathroom	Unit B OccupancyZoneName
B105	Room	Level 1	4.92	10.50	5.70	20.8	Stairway	Unit B OccupancyZoneName
A201	Hallway	Level 2	7.80	15.32	2.90	18.1	General Residential Space	Unit A OccupancyZoneName
A202	Bedroom 1	Level 2	26.12	21.42	2.60	56.9	Bedroom	Unit A OccupancyZoneName
A203	Bedroom 2	Level 2	26.18	21.48	2.60	56.9	Bedroom	Unit A OccupancyZoneName
A204	Bathroom 2	Level 2	5.42	9.84	2.60	12.2	Bathroom	Unit A OccupancyZoneName
A205	Utility	Level 2	1.75	5.43	2.60	3.7	Service Distribution Spaces	Unit A OccupancyZoneName
B201	Hallway	Level 2	7.80	15.32	2.90	18.1	General Residential Space	Unit B OccupancyZoneName
B202	Bedroom 1	Level 2	26.12	21.42	2.60	56.9	Bedroom	Unit B OccupancyZoneName
B203	Bedroom 2	Level 2	26.18	21.91	2.60	56.9	Bedroom	Unit B OccupancyZoneName
B204	Bathroom 2	Level 2	5.44	9.87	2.60	12.3	Bathroom	Unit B OccupancyZoneName
B205	Utility	Level 2	1.73	5.40	2.60	3.6	Service Distribution Spaces	Unit B OccupancyZoneName
R301	Roof	Roof	145.72	51.53	3.00	405.5	Other General Facility Service Spaces	Roof OccupancyZoneName

Areas, perimeters and volumes as computed by the authoring tool and stored in the model.

CODE REVIEW 3D · SAMPLE MODEL

Duplex Apartment

Residential

SHEET

Room schedule

SHEET NO.

A-601

of 6 sheets

SCALE

Not to scale

SUMMARY

Rooms	**21**
Net area, floors	**276.3 m²**
Area on Level 1	**141.8 m²**
Area on Level 2	**134.5 m²**
Area on Roof	**145.7 m²**

SOURCE

BSI (2020) "Duplex Apartment Test Files," buildingSMART International. License: CC BY 4.0.

Changes: drawings generated from the 3D model (duplex.ifc); the model itself is unchanged.

NOTES

Generated automatically from the IFC model for review demos. Not a construction document. Check the scale bar before measuring from a print.

Generated 2026-10-24 with IfcOpenShell
apps/review/scripts/make_drawings.py

DOOR SCHEDULE

Mark	Level	From / to	Type	Type mark	Width (mm)	Height (mm)	Leaf (mm)	Operation	External	Fire rating
A101	Level 1	A101 Foyer	1250mm x 2010mm	33	1250	2010	51	single swing right	Yes	—
A102	Level 1	A102 Living Room	0813 x 2420mm	56	813	2420	51	single swing left	Yes	—
A104	Level 1	A101 Foyer / A104 Bathroom 1	0762 x 2032mm	28	762	2032	51	single swing left	No	—
B101	Level 1	B101 Foyer	1250mm x 2010mm	33	1250	2010	51	single swing right	Yes	—
B102	Level 1	B102 Living Room	0813 x 2420mm	56	813	2420	51	single swing left	Yes	—
B104	Level 1	B101 Foyer / B104 Bathroom 1	0762 x 2032mm	28	762	2032	51	single swing left	No	—
A202	Level 2	A201 Hallway / A202 Bedroom 1	0864 x 2032mm	32	864	2032	51	single swing left	No	—
A203	Level 2	A201 Hallway / A203 Bedroom 2	0864 x 2032mm	32	864	2032	51	single swing right	No	—
A204	Level 2	A201 Hallway / A204 Bathroom 2	0864 x 2032mm	32	864	2032	51	single swing right	No	—
A205	Level 2	A201 Hallway / A204 Bathroom 2 / A205 Utility	0762 x 2032mm	28	762	2032	51	single swing right	No	—
B202	Level 2	B201 Hallway / B202 Bedroom 1	0864 x 2032mm	32	864	2032	51	single swing left	No	—
B203	Level 2	B201 Hallway / B203 Bedroom 2	0864 x 2032mm	32	864	2032	51	single swing right	No	—
B204	Level 2	B201 Hallway / B204 Bathroom 2	0864 x 2032mm	32	864	2032	51	single swing right	No	—
B205	Level 2	B204 Bathroom 2 / B205 Utility	0762 x 2032mm	28	762	2032	51	single swing right	No	—

Width and height are the overall door sizes in the model, not the clear opening width used for egress checks.
"From / to" lists the rooms the model records on each side of the door; one room means an exterior door or a missing boundary.
Fire ratings are blank in the source model.

CODE REVIEW 3D · SAMPLE MODEL

Duplex Apartment

Residential

SHEET

Door schedule

SHEET NO.

A-611

of 6 sheets

SCALE

Not to scale

SUMMARY

Doors	14
External doors	4
Door types	4
Without room links	0

SOURCE

BSI (2020) "Duplex Apartment Test Files," buildingSMART International. License: CC BY 4.0.

Changes: drawings generated from the 3D model (duplex.ifc); the model itself is unchanged.

NOTES

Generated automatically from the IFC model for review demos. Not a construction document. Check the scale bar before measuring from a print.

WINDOW SCHEDULE

Mark	Level	Room	Type	Type mark	Width (mm)	Height (mm)	Sill (mm)	Head (mm)	External
10	Level 1	A102 Living Room	4835mm x 2420mm	05	4835	2420	100	2520	Yes
12	Level 1	B102 Living Room / B103 Kitchen	750mm x 2200mm	04	750	2200	100	2300	Yes
13	Level 1	A102 Living Room / A103 Kitchen	750mm x 2200mm	04	750	2200	100	2300	Yes
9	Level 1	B102 Living Room	4835mm x 2420mm	05	4835	2420	100	2520	Yes
14	Level 2	B203 Bedroom 2	2800mm x 2410mm	01	2800	2410	100	2510	Yes
15	Level 2	B203 Bedroom 2	819mm x 759mm	02	819	759	100	859	Yes
16	Level 2		819mm x 759mm	03	819	759	925	1684	Yes
17	Level 2		819mm x 759mm	02	819	759	1751	2510	Yes
18	Level 2	A203 Bedroom 2	2800mm x 2410mm	01	2800	2410	100	2510	Yes
19	Level 2	A203 Bedroom 2	819mm x 759mm	02	819	759	100	859	Yes
20	Level 2		819mm x 759mm	03	819	759	926	1684	Yes
21	Level 2		819mm x 759mm	02	819	759	1751	2510	Yes
22	Level 2	B202 Bedroom 1	2800mm x 2410mm	01	2800	2410	100	2510	Yes
23	Level 2		819mm x 759mm	02	819	759	1751	2510	Yes
24	Level 2	B202 Bedroom 1	819mm x 759mm	02	819	759	100	859	Yes
25	Level 2		819mm x 759mm	03	819	759	926	1684	Yes
26	Level 2	A202 Bedroom 1	2800mm x 2410mm	01	2800	2410	100	2510	Yes
27	Level 2		819mm x 759mm	02	819	759	1751	2510	Yes
28	Level 2		819mm x 759mm	03	819	759	926	1684	Yes
29	Level 2	A202 Bedroom 1	819mm x 759mm	02	819	759	100	859	Yes
31	Level 2	A203 Bedroom 2	750mm x 2200mm	04	750	2200	100	2300	Yes
32	Level 2	B203 Bedroom 2	750mm x 2200mm	04	750	2200	100	2300	Yes
33	Roof		1180 x 1170mm	36	1173	635		635	No
34	Roof		1180 x 1170mm	36	1173	635		635	No

Sill and head heights are measured from the finished floor of the window's level.

CODE REVIEW 3D · SAMPLE MODEL

Duplex Apartment

Residential

SHEET

Window schedule

SHEET NO.

A-621

of 6 sheets

SCALE

Not to scale

SUMMARY

Windows	**24**
Window types	**5**

SOURCE

BSI (2020) "Duplex Apartment Test Files," buildingSMART International. License: CC BY 4.0.

Changes: drawings generated from the 3D model (duplex.ifc); the model itself is unchanged.

NOTES

Generated automatically from the IFC model for review demos. Not a construction document. Check the scale bar before measuring from a print.